

F1S-201_UPPERWISHBONE
4130 WELDED, QTY 1, 1323 g (INVENTOR)
SCALE 1:2.5

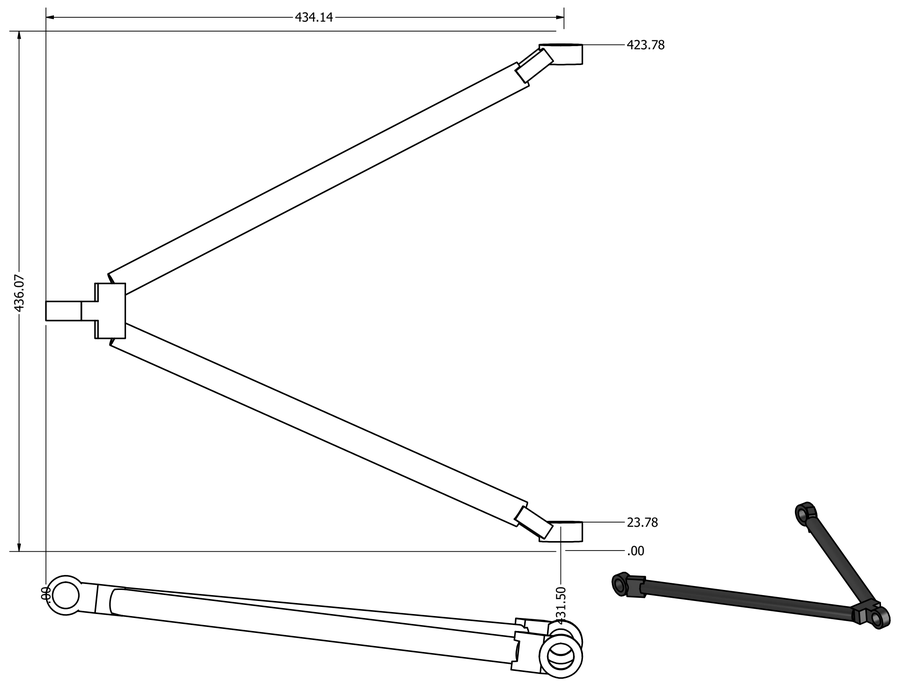


F1S-202_LOWERWISHBONE
4130 WELDED, QTY 1, 1930 g (INVENTOR)
SCALE 1:3

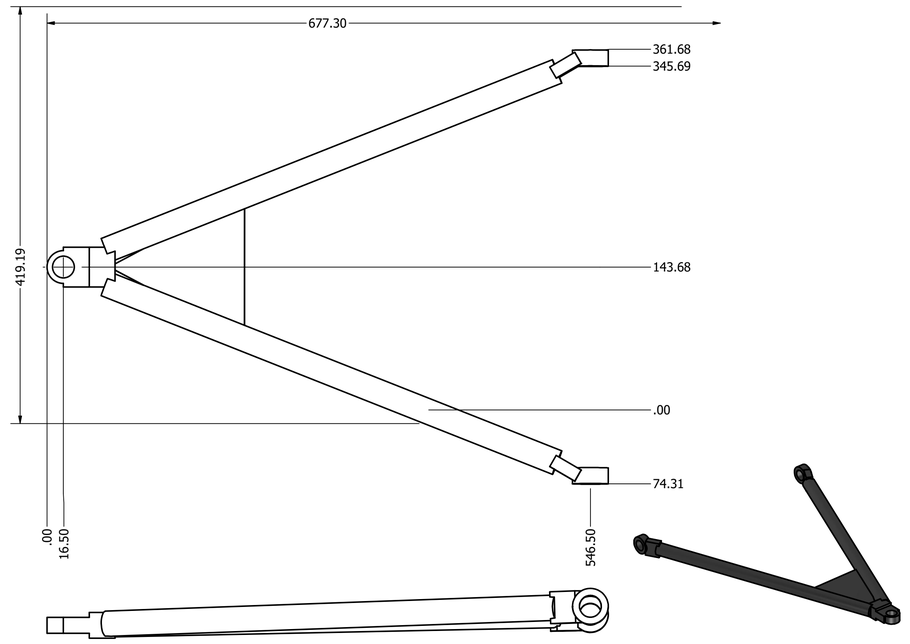


NOTES:
1. 4130: NORMALISED TUBE, TIG WELD (ER80S-D2), NORMALISE AFTER WELDING, MPI 100% OF WELDS.
2. 7075-T6: MACHINE FROM PLATE/BILLET, BREAK SHARP EDGES 0.5, HARD ANODISE (TYPE III) AFTER MACHINING.
3. GE 12 E BEARING BORES 22 H7, STAKE BOTH SIDES. BOLT HOLES 12 H8 (M12 12.9 SHANK). M8 INSERT HOLES TO SUIT.
4. UNTOLERANCED DIMS +/-0.2 MM (MACHINED), +/-0.5 MM (WELDED, AFTER JIG). HARDPOINTS ON JIG +/-0.1 MM.
5. ALL DIMENSIONS MM, PARTS MODELLED IN CAR COORDINATES (X FWD, Y LEFT, Z UP). SOURCE: _build/design.py + build_parts.py.


DRAWN Jay Patel	10/28/2026	
CHECKED		TITLE F1Suspension - part manufacturing drawings
QA		
MFG		
APPROVED		
		SIZE D · DWG NO F1S-DWG-100 · REV
		SCALE 0.40 : 1 · SHEET 1 OF 4


F1S-203 UPRIGHT
7075-T6, QTY 1, 3033 g (INVENTOR)
SCALE 1:2

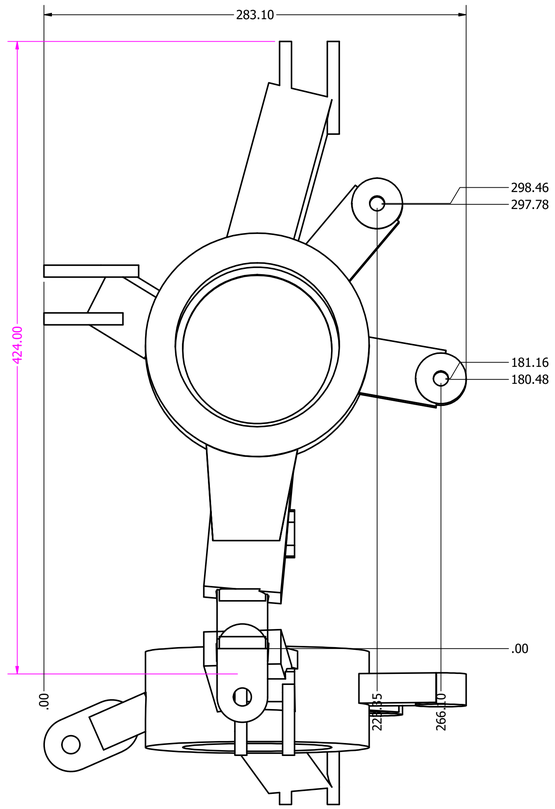

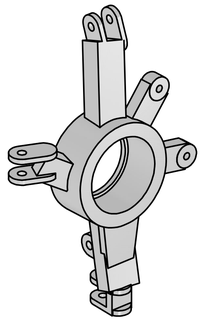

F1S-206 ROCKER
7075-T6, QTY 1, 310 g (INVENTOR)
SCALE 1:1

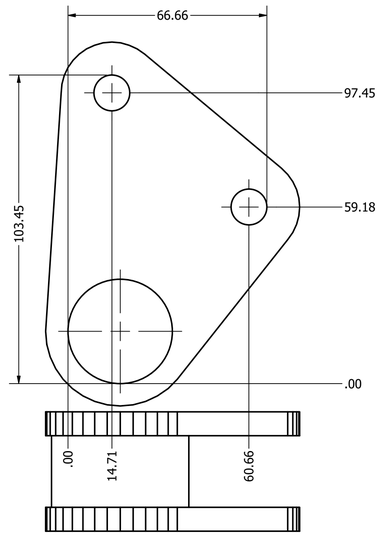


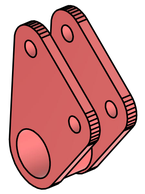


NOTES:
1. 4130: NORMALISED TUBE, TIG WELD (ER80S-D2), NORMALISE AFTER WELDING, MPI 100% OF WELDS.
2. 7075-T6: MACHINE FROM PLATE/BILLET, BREAK SHARP EDGES 0.5, HARD ANODISE (TYPE III) AFTER MACHINING.
3. GE 12 E BEARING BORES 22 H7, STAKE BOTH SIDES. BOLT HOLES 12 H8 (M12 12.9 SHANK). M8 INSERT HOLES TO SUIT.
4. UNTOLERANCED DIMS +/-0.2 MM (MACHINED), +/-0.5 MM (WELDED, AFTER JIG). HARDPOINTS ON JIG +/-0.1 MM.
5. ALL DIMENSIONS MM, PARTS MODELLED IN CAR COORDINATES (X FWD, Y LEFT, Z UP). SOURCE: _build/design.py + build_parts.py.


DRAWN Jay Patel	10/28/2026	
CHECKED		TITLE F1Suspension - part manufacturing drawings
QA		
MFG		
APPROVED		SIZE D · DWG NO F1S-DWG-100 · REV
		SCALE 1 / 2 · SHEET 2 OF 4


F1S-101 ~~WISHBONECLEVIS~~
7075-T6, QTY 5, 155 g (INVENTOR)
SCALE 1:1

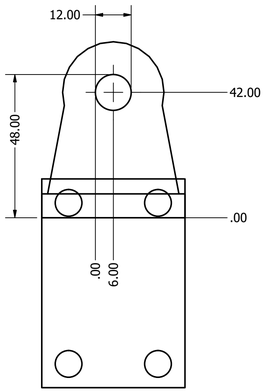

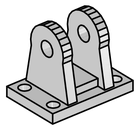


F1S-102 ~~ROCKERMOUNT~~
7075-T6, QTY 1, 208 g (INVENTOR)
SCALE 1:1

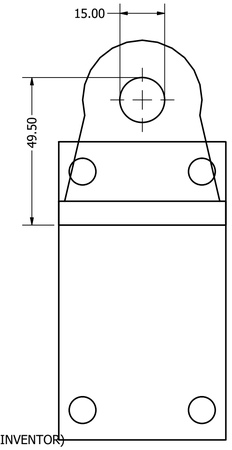

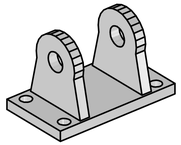


F1S-204 ~~PUSHROD~~
4130, QTY 1, 846 g (INVENTOR)
SCALE 1:6

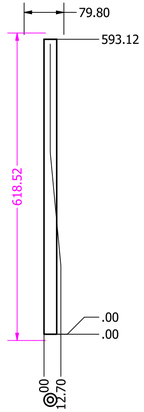


F1S-205 TIEROD
4130, QTY 1, 434 g (INVENTOR)
SCALE 1:4



F1S-104 RACKBAR
17-4PH, QTY 1, 1043 g (INVENTOR)
SCALE 1:4

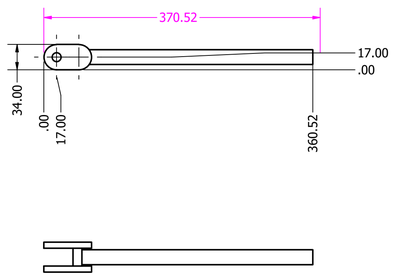


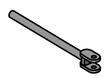


NOTES:
1. 4130: NORMALISED TUBE, TIG WELD (ER80S-D2), NORMALISE AFTER WELDING, MPI 100% OF WELDS.
2. 7075-T6: MACHINE FROM PLATE/BILLET, BREAK SHARP EDGES 0.5, HARD ANODISE (TYPE III) AFTER MACHINING.
3. GE 12 E BEARING BORES 22 H7, STAKE BOTH SIDES. BOLT HOLES 12 H8 (M12 12.9 SHANK). M8 INSERT HOLES TO SUIT.
4. UNTOLERANCED DIMS +/-0.2 MM (MACHINED), +/-0.5 MM (WELDED, AFTER JIG). HARDPOINTS ON JIG +/-0.1 MM.
5. ALL DIMENSIONS MM, PARTS MODELLED IN CAR COORDINATES (X FWD, Y LEFT, Z UP). SOURCE: _build/design.py + build_parts.py.


DRAWN Jay Patel	10/28/2026		
CHECKED		TITLE	F1Suspension - part manufacturing drawings
QA			
MFG			
APPROVED		SIZE D	DWG NO F1S-DWG-100 REV
		SCALE 1 : 1	SHEET 3 OF 4

F1S-401 HUB
TI-6AL-4V, QTY 1, 3066 g (INVENTOR)
SCALE 1:2

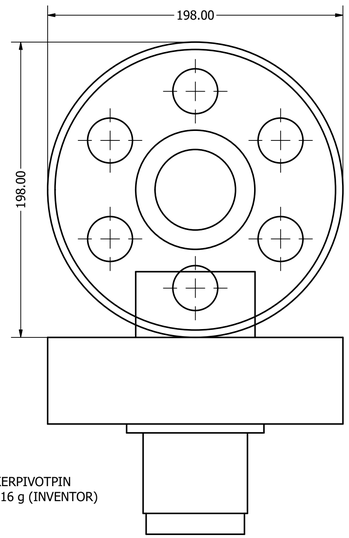

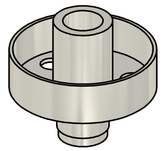


F1S-515 ROCKERPIVOTPIN
4340, QTY 1, 116 g (INVENTOR)
SCALE 1:1

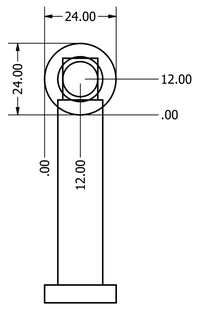




F1S-483 HUBNUT
4340, QTY 1, 290 g (INVENTOR)
SCALE 1:1

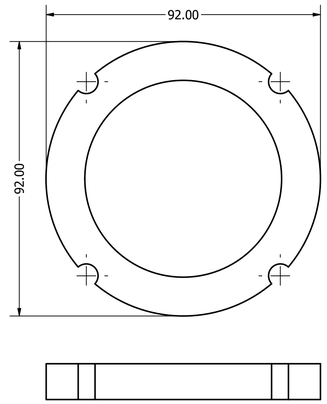





F1S-519 SPACER12X7C
17-4PH, QTY 16, 5 g (INVENTOR)
SCALE 1:1

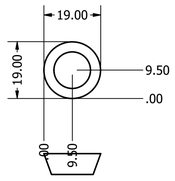



F1S-488 WHEELNUT
7075-T6, QTY 1, 301 g (INVENTOR)
SCALE 1:1.5

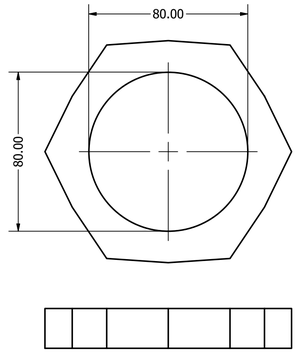

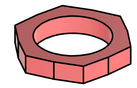

NOTES:
1. 4130: NORMALISED TUBE, TIG WELD (ER80S-D2), NORMALISE AFTER WELDING, MPI 100% OF WELDS.
2. 7075-T6: MACHINE FROM PLATE/BILLET, BREAK SHARP EDGES 0.5, HARD ANODISE (TYPE III) AFTER MACHINING.
3. GE 12 E BEARING BORES 22 H7, STAKE BOTH SIDES. BOLT HOLES 12 H8 (M12 12.9 SHANK). M8 INSERT HOLES TO SUIT.
4. UNTOLERANCED DIMS +/-0.2 MM (MACHINED), +/-0.5 MM (WELDED, AFTER JIG). HARDPOINTS ON JIG +/-0.1 MM.
5. ALL DIMENSIONS MM, PARTS MODELLED IN CAR COORDINATES (X FWD, Y LEFT, Z UP). SOURCE: _build/design.py + build_parts.py.

DRAWN Jay Patel	10/28/2026	
CHECKED		TITLE F1Suspension - part manufacturing drawings
QA		
MFG		
APPROVED		
		SIZE D · DWG NO F1S-DWG-100 · REV
		SCALE 1 / 2 · SHEET 4 OF 4